

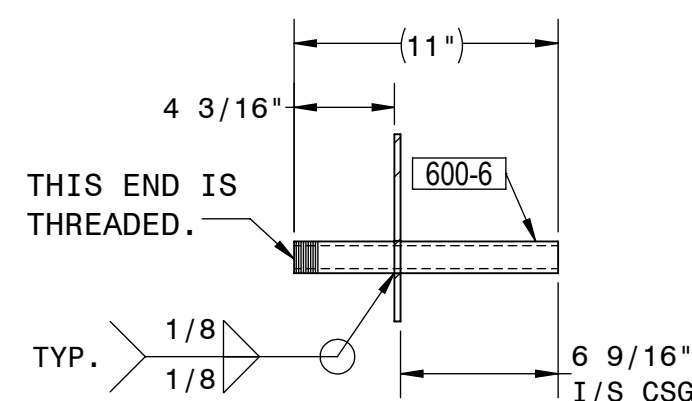
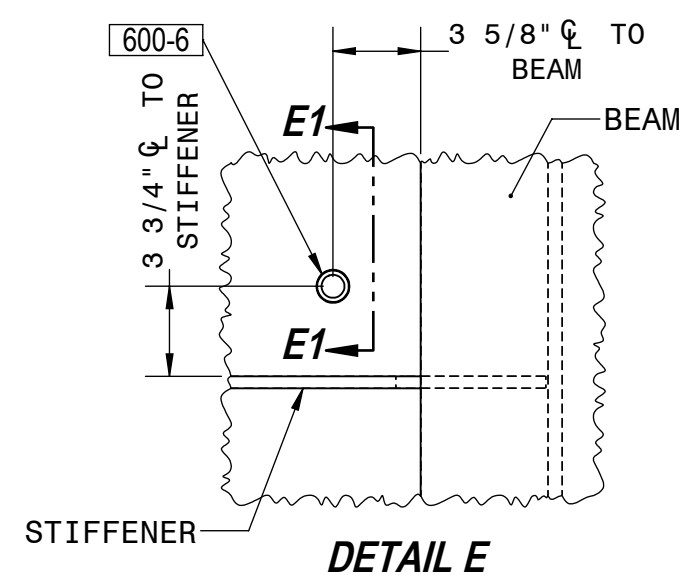
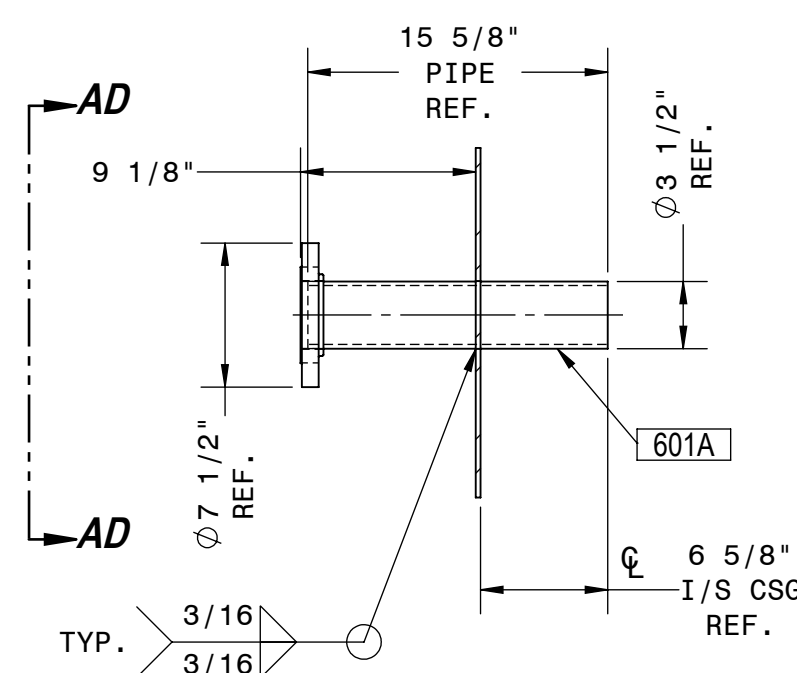
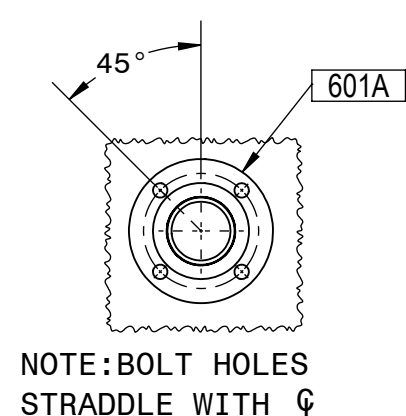
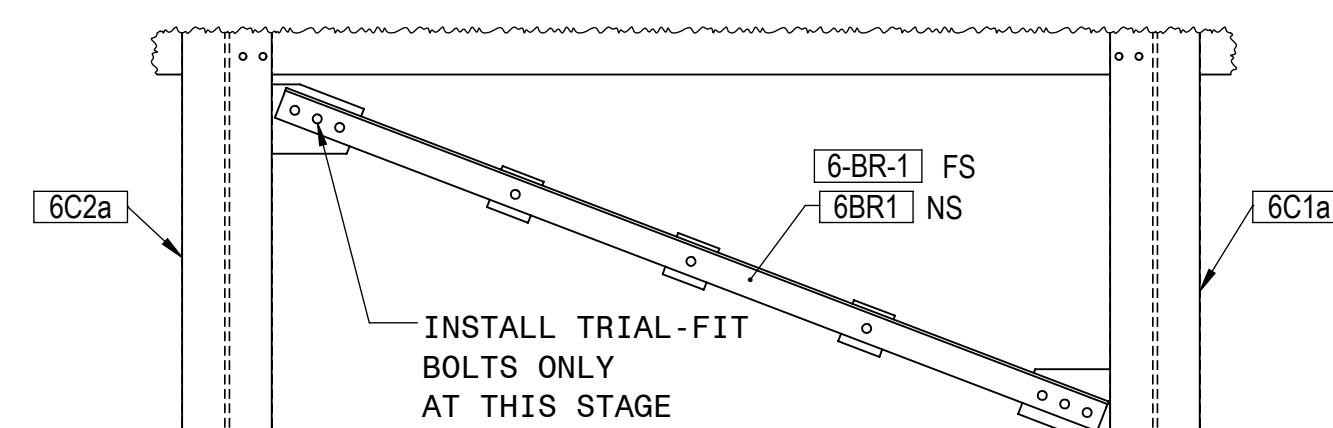
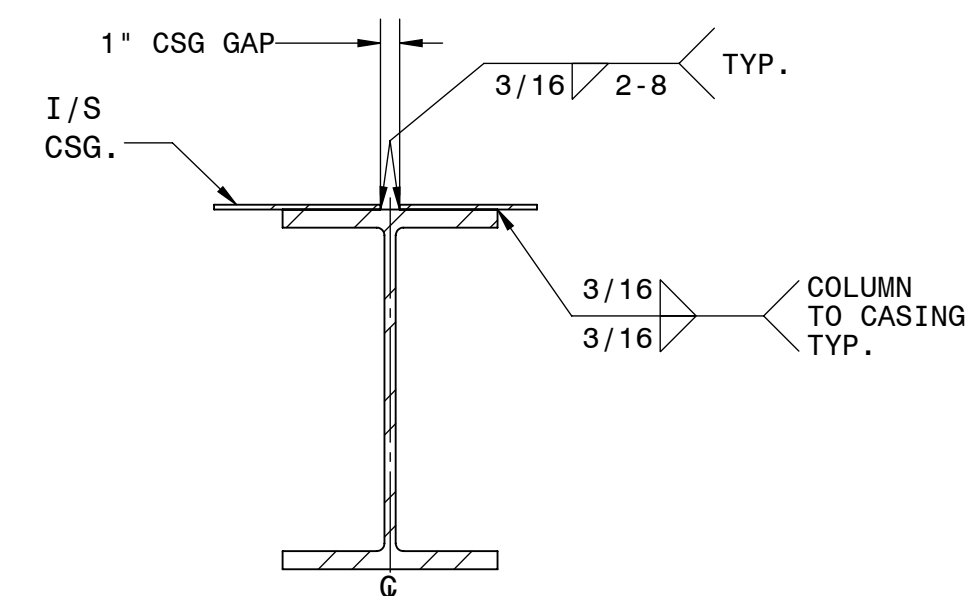
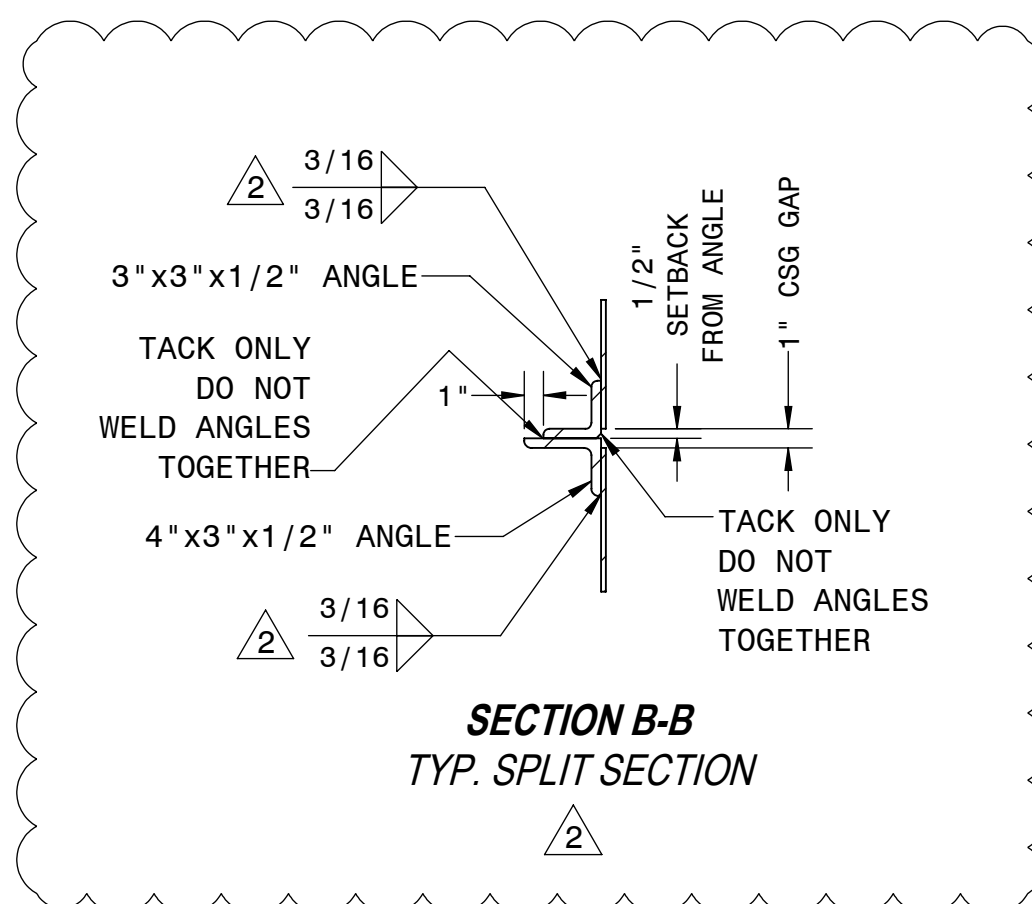
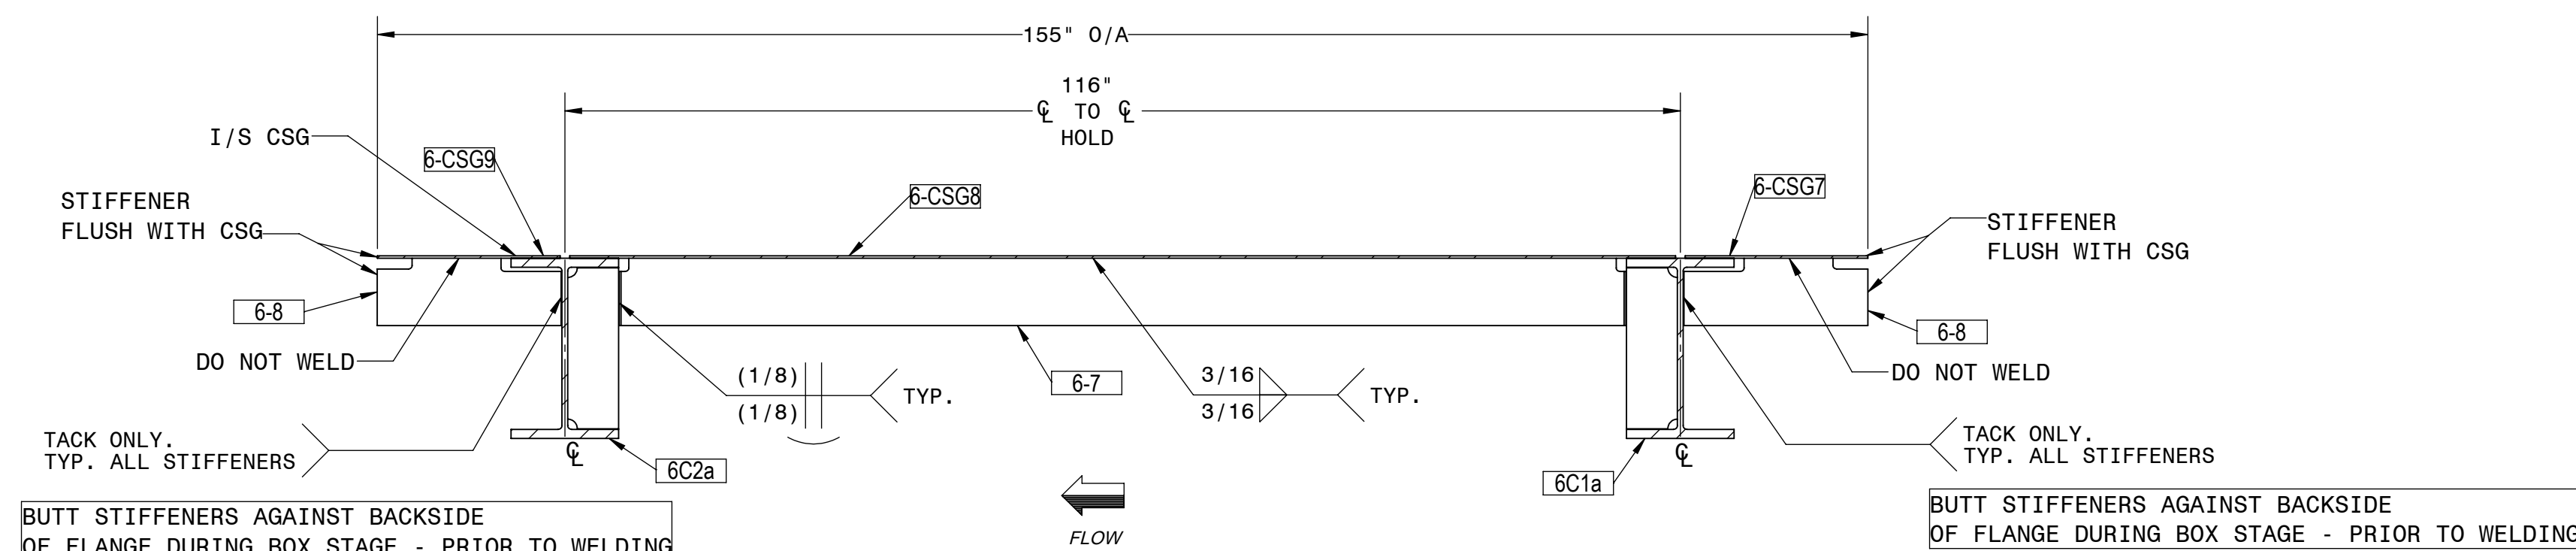


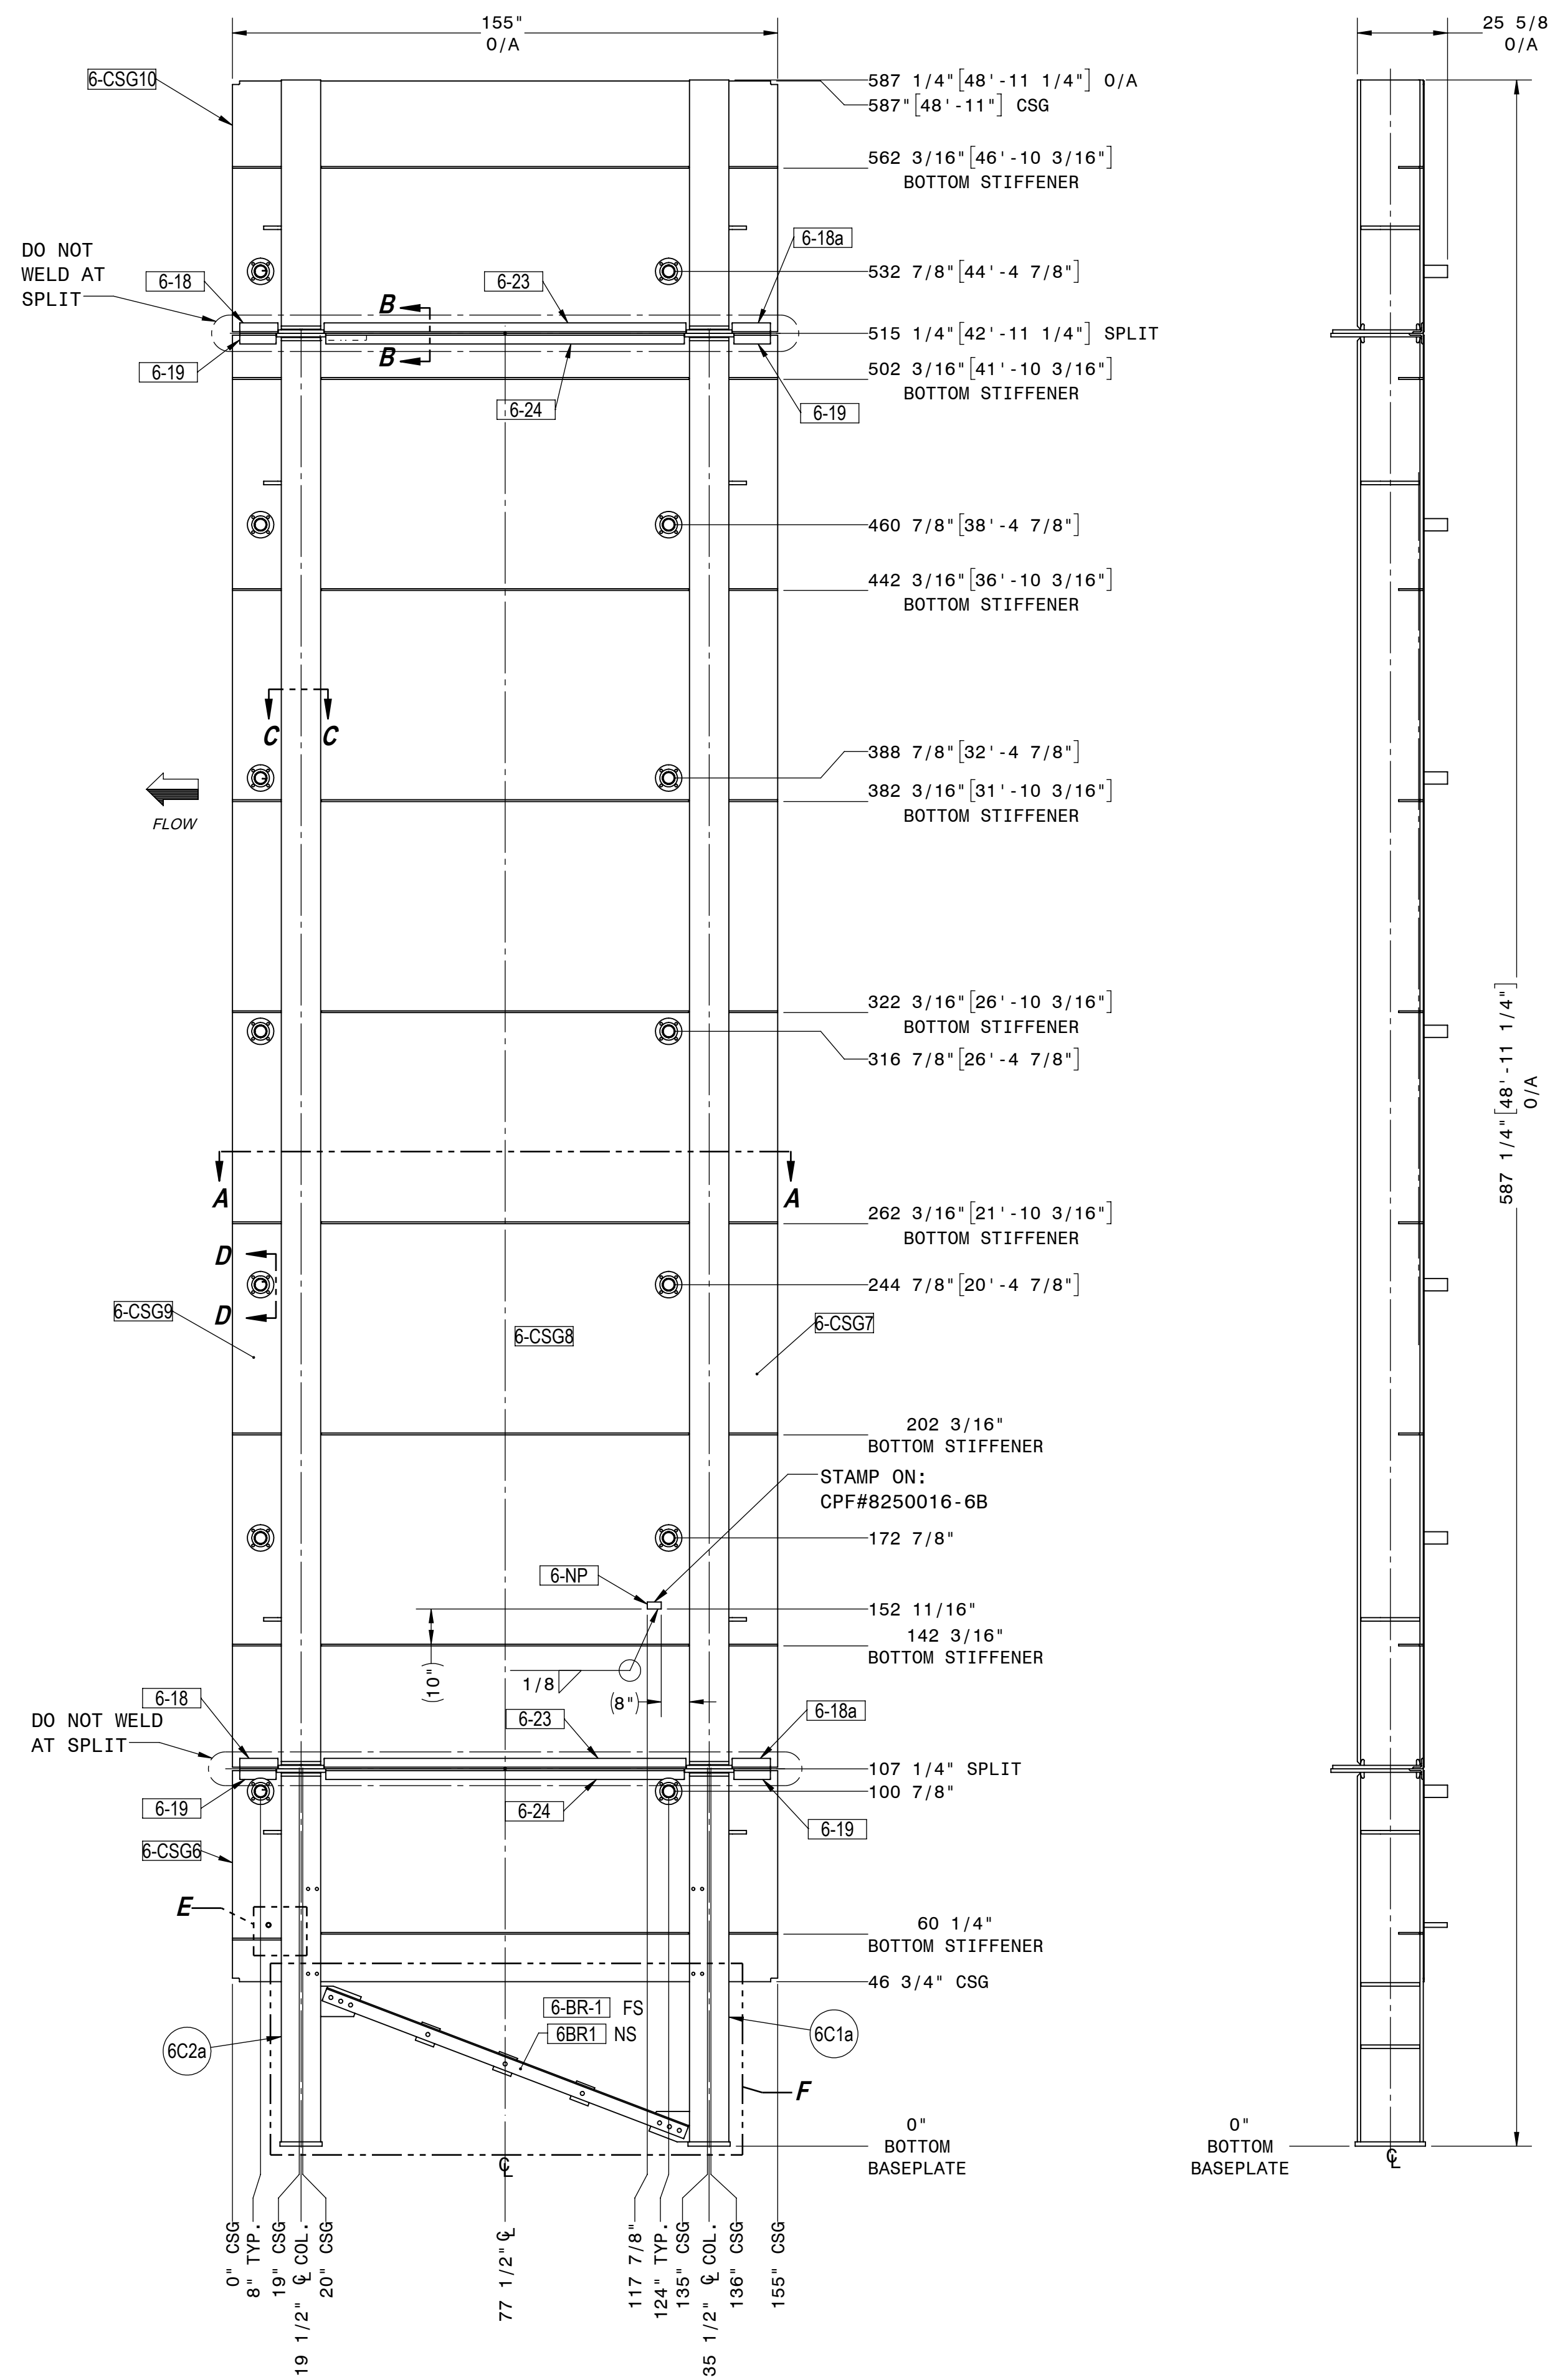

WELDMENT SIGN OFF'S				
PANEL #	FIT	QA	WELD	QA

2	WELD SYMBOL NOTES REMOVED FROM SECTION B-B	FEB-17-2026	AD	KA
1	PART #600-6, DETAIL E & SECTION E1-E1 ADDED.	FEB-03-2026	OD	KA
0	ISSUED FOR FABRICATION	AUG-11-2025	OD	KA
REV.	DESCRIPTION	DATE	BY	CHKD

	THIS DRAWING IS THE PROPERTY OF CAMBRIDGE PRO FAB INC. AND IS NOT TO BE REPRODUCED OR TRANSMITTED IN ANY FORM OR BY ANY MEANS, ELECTRONIC OR MECHANICAL, INCLUDING PHOTOCOPYING, RECORDING, OR BY ANY INFORMATION STORAGE AND RETRIEVAL SYSTEM.		CUSTOMER	
	TOLERANCES PER MMSP-01 CUSTOMER SPECS OVERIDE MMSP-01		GE-VALMY NV - 2SCR SYSTEMS	
CAMBRIDGE PRO FAB INC.	TITLE		SCR DUCT FAR SIDE PANEL WELDMENT BOX 6	
84 SHAWNEE STREET BRANTFORD ONTARIO CANADA N3R 1C6	DWN SD DATE APR-30-2025	CHKD KA WEIGHT 20973 lbs	SHT No 1 OF 2	WID No 8250016
				DWG No 681
				REV 2

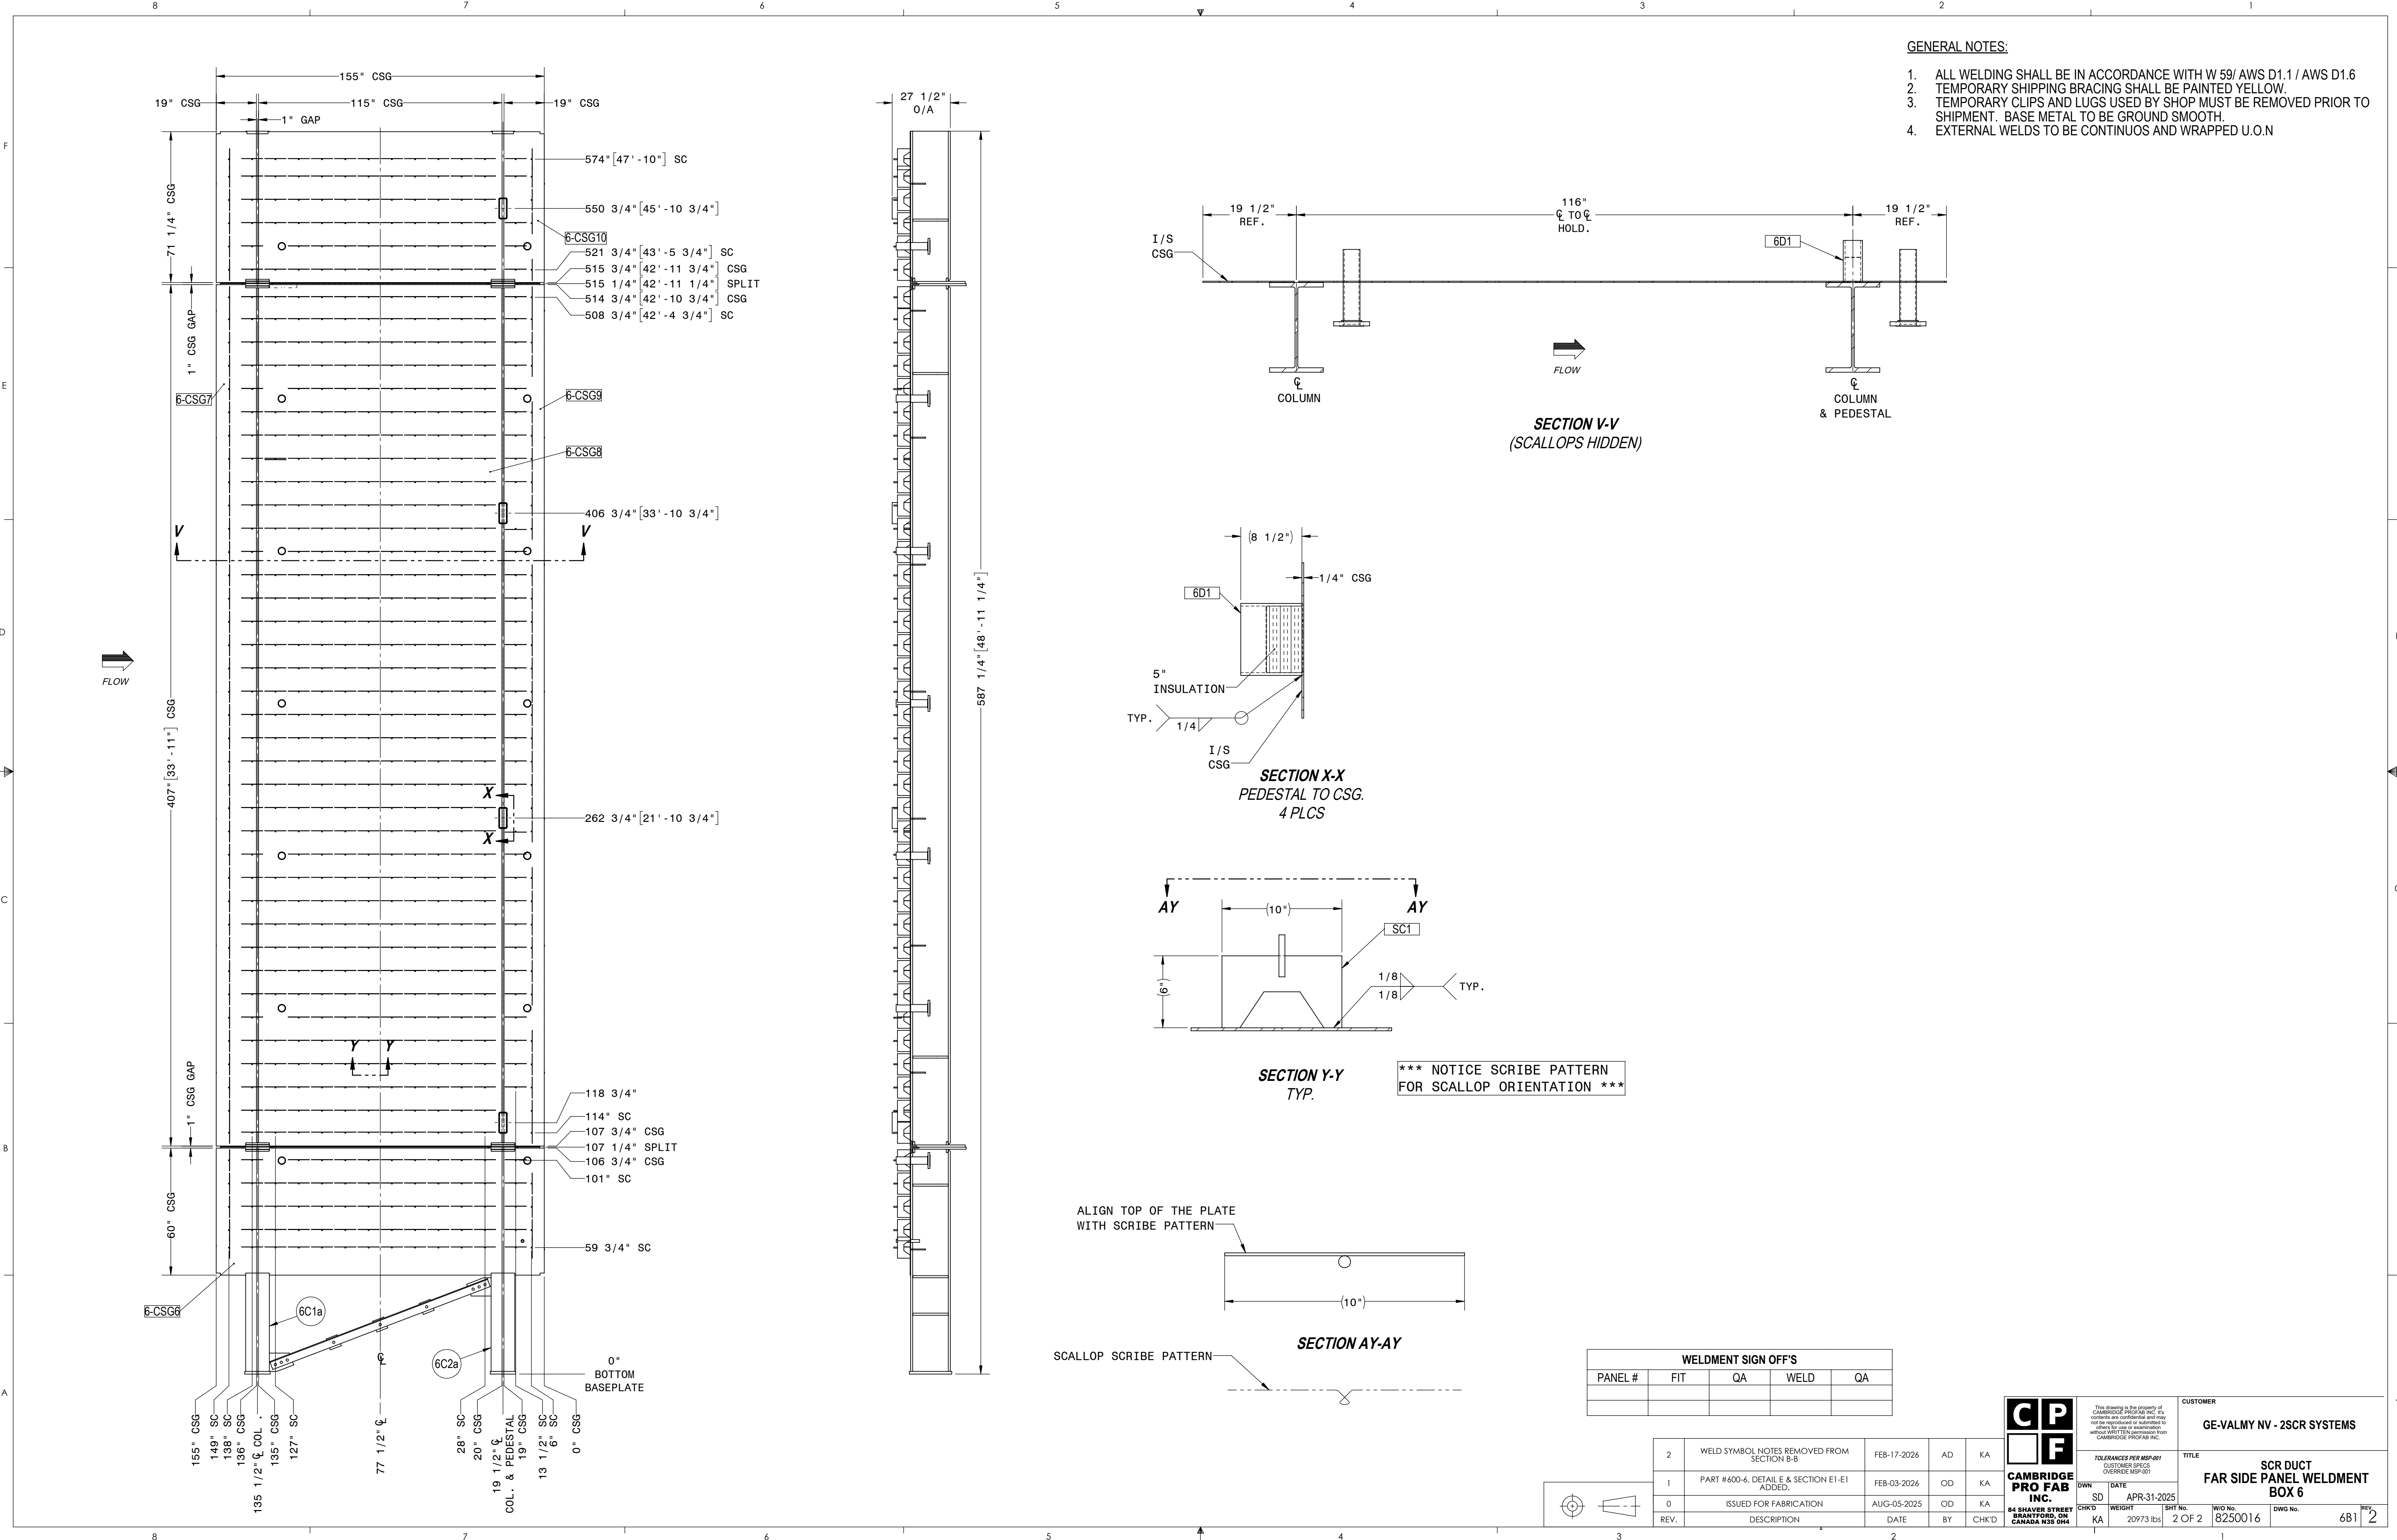

GENERAL NOTES:

1. ALL WELDING SHALL BE IN ACCORDANCE WITH W 59/ AWS D1.1 / AWS D1.6
2. TEMPORARY SHIPPING BRACING SHALL BE PAINTED YELLOW.
3. TEMPORARY CLIPS AND LUGS USED BY SHOP MUST BE REMOVED PRIOR TO SHIPMENT. BASE METAL TO BE GROUND SMOOTH.
4. EXTERNAL WELDS TO BE CONTINUOUS AND WRAPPED U.O.N

CP
F

CAMBRIDGE
PRO FAB
INC.
84 SHAVER STREET
BRANTFORD, ON
CANADA N3S 0H4

This drawing is the property of
CAMBRIDGE PRO FAB INC. It's
contents are confidential and may
not be reproduced or submitted to
others for use or examination
without written permission from
CAMBRIDGE PRO FAB INC.

DWN	SD	DATE	SHT No.	WIO No.	DWG No.
KA	KA	APR-31-2025	2 OF 2	8250016	6B1

CUSTOMER	
GE-VALMY NV - 2SCR SYSTEMS	
TITLE	
SCR DUCT FAR SIDE PANEL WELDMENT BOX 6	